
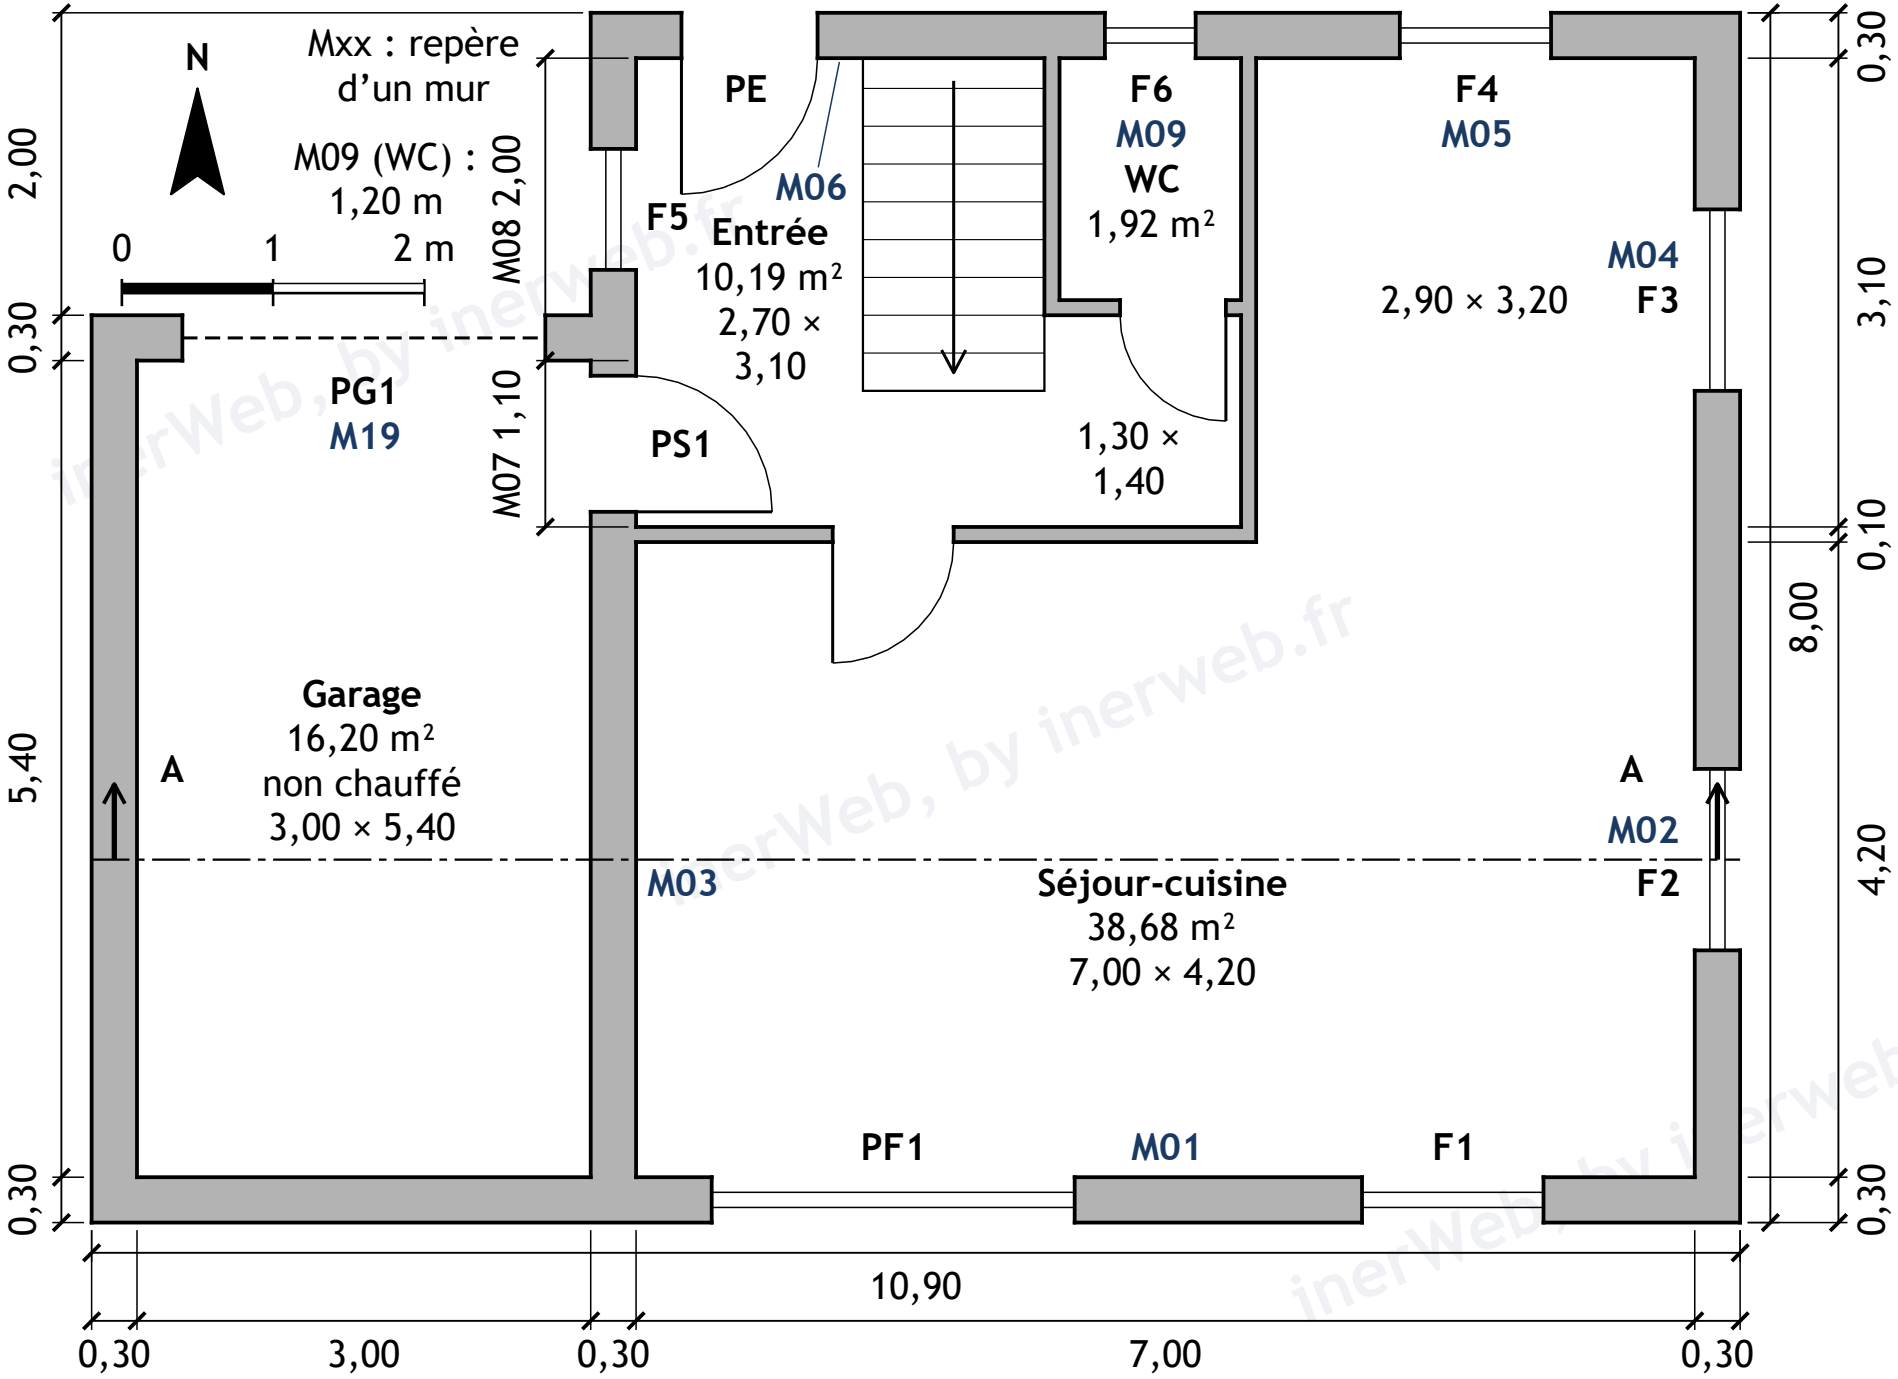


inerWeb, by inerweb.fr

inerWeb **Bureau d'études** **Plan du rez-de-chaussée** Maison d'étude BE, Marseille, zone H3


Échelle 1/50 Cotes en mètres 08/11/2026 Plan généré depuis maison.json, version 2

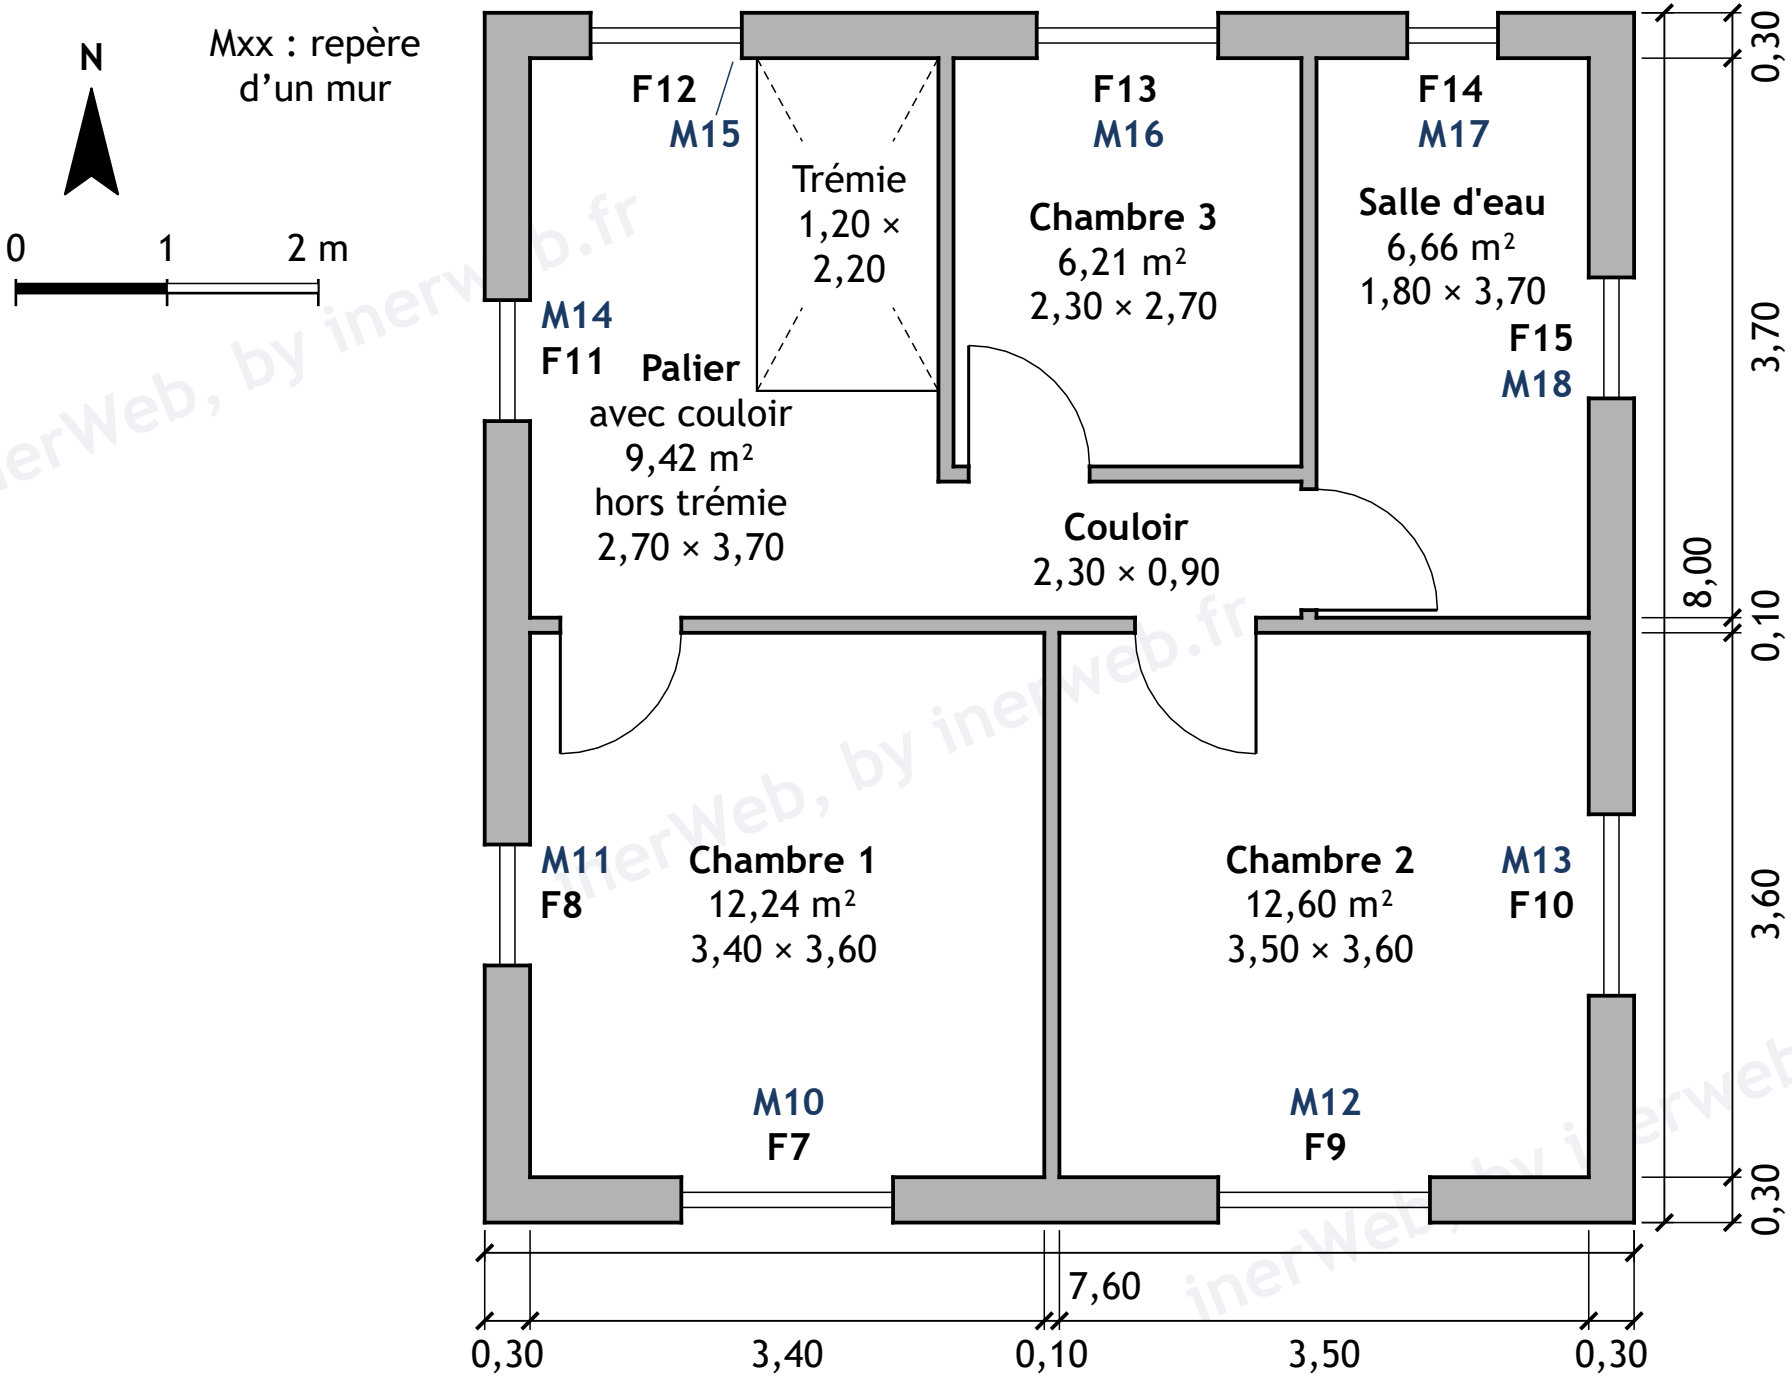

inerWeb, by inerWeb.fr


inerWeb **Bureau d'études** **Plan de l'étage** Maison d'étude BE, Marseille, zone H3

Échelle 1/50 Cotes en mètres 08/11/2026 Plan généré depuis maison.json, version 2

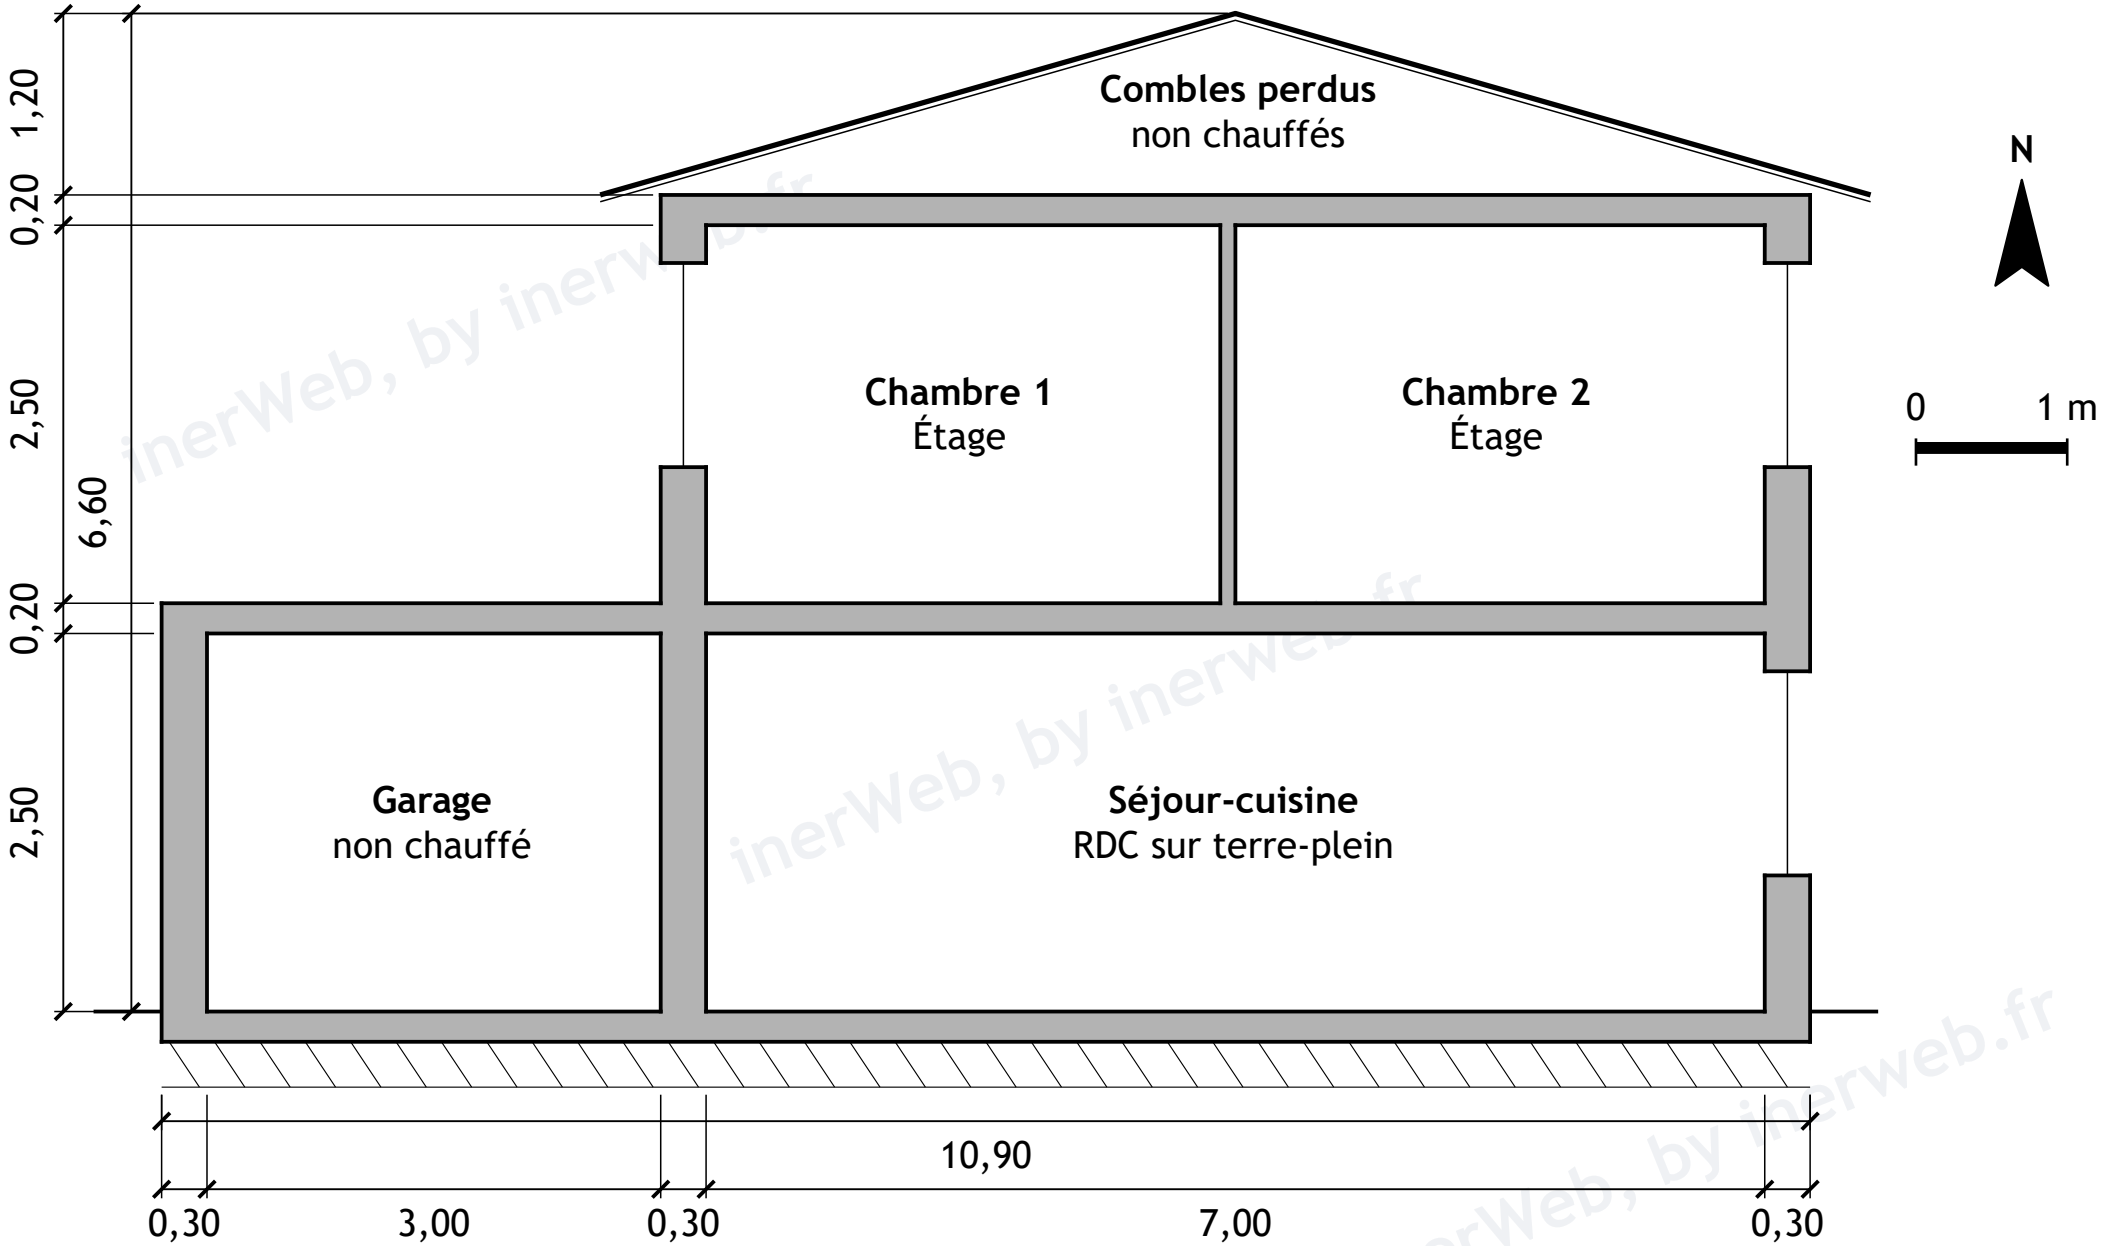


inerWeb, by inerweb.fr

inerWeb	Bureau d'études	**Coupe A-A**		Maison d'étude BE, Marseille, zone H3
Échelle 1/50	Cotes en mètres	08/11/2026	Plan généré depuis maison.json, version 2	

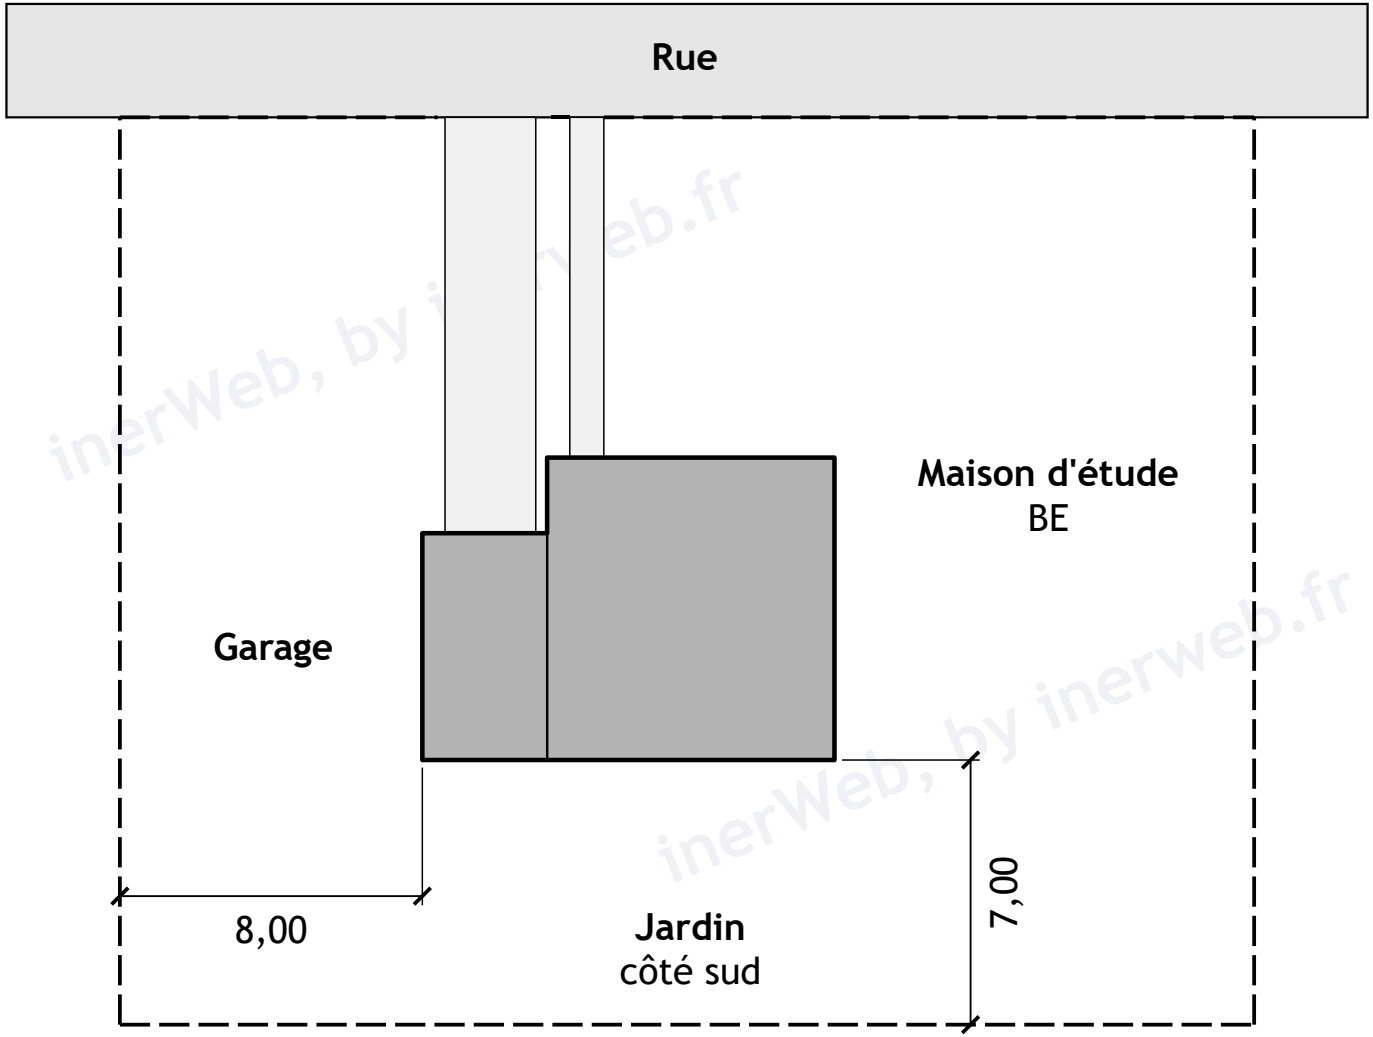



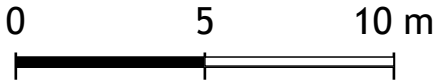

Marseille
Zone H3
Altitude 0 m

inerWeb, by inerweb.fr

inerWeb	Bureau d'études	**Plan de masse**		Maison d'étude BE, Marseille, zone H3
Échelle 1/200	Cotes en mètres	08/11/2026	Plan généré depuis maison.json, version 2	

Repère	Type	Larg.	Haut.	Allège	Pièce	Niveau	Mur	Orient.
PF1	Porte-fenêtre 2 vantaux	2,40	2,15	0,00	Séjour-cuisine	RDC	M01	Sud
F1	Fenêtre 2 vantaux	1,20	1,35	0,90	Séjour-cuisine	RDC	M01	Sud
F2	Fenêtre 2 vantaux	1,20	1,35	0,90	Séjour-cuisine	RDC	M02	Est
F3	Fenêtre 2 vantaux	1,20	1,35	0,90	Séjour-cuisine	RDC	M04	Est
F4	Fenêtre 1 vantail	1,00	1,35	0,90	Séjour-cuisine	RDC	M05	Nord
PE	Porte d'entrée pleine	0,90	2,10	0,00	Entrée	RDC	M06	Nord
PS1	Porte de service vers le garage	0,90	2,10	0,00	Entrée	RDC	M07	Ouest
F5	Fenêtre 1 vantail	0,80	1,35	0,90	Entrée	RDC	M08	Ouest
F6	Fenêtre oscillo-battante	0,60	0,60	1,40	WC	RDC	M09	Nord
PG1	Porte de garage sectionnelle	2,40	2,00	0,00	Garage	RDC	M19	Nord
F7	Fenêtre 2 vantaux	1,40	1,35	0,90	Chambre 1	Étage	M10	Sud
F8	Fenêtre 1 vantail	0,80	1,35	0,90	Chambre 1	Étage	M11	Ouest
F9	Fenêtre 2 vantaux	1,40	1,35	0,90	Chambre 2	Étage	M12	Sud
F10	Fenêtre 2 vantaux	1,20	1,35	0,90	Chambre 2	Étage	M13	Est
F11	Fenêtre 1 vantail	0,80	1,35	0,90	Palier	Étage	M14	Ouest
F12	Fenêtre 1 vantail	1,00	1,35	0,90	Palier	Étage	M15	Nord
F13	Fenêtre 2 vantaux	1,20	1,35	0,90	Chambre 3	Étage	M16	Nord
F14	Fenêtre oscillo-battante	0,60	0,60	1,40	Salle d'eau	Étage	M17	Nord
F15	Fenêtre 1 vantail	0,80	1,00	1,10	Salle d'eau	Étage	M18	Est

Largeur, hauteur et allège en mètres, dimensions de tableau.
L'allège est la hauteur entre le sol fini et le bas de la baie. Les portes ont une allège nulle.
Orientation : celle de la face extérieure du mur. Les portes intérieures ne sont pas relevées.

inerWeb, by inerweb.fr