
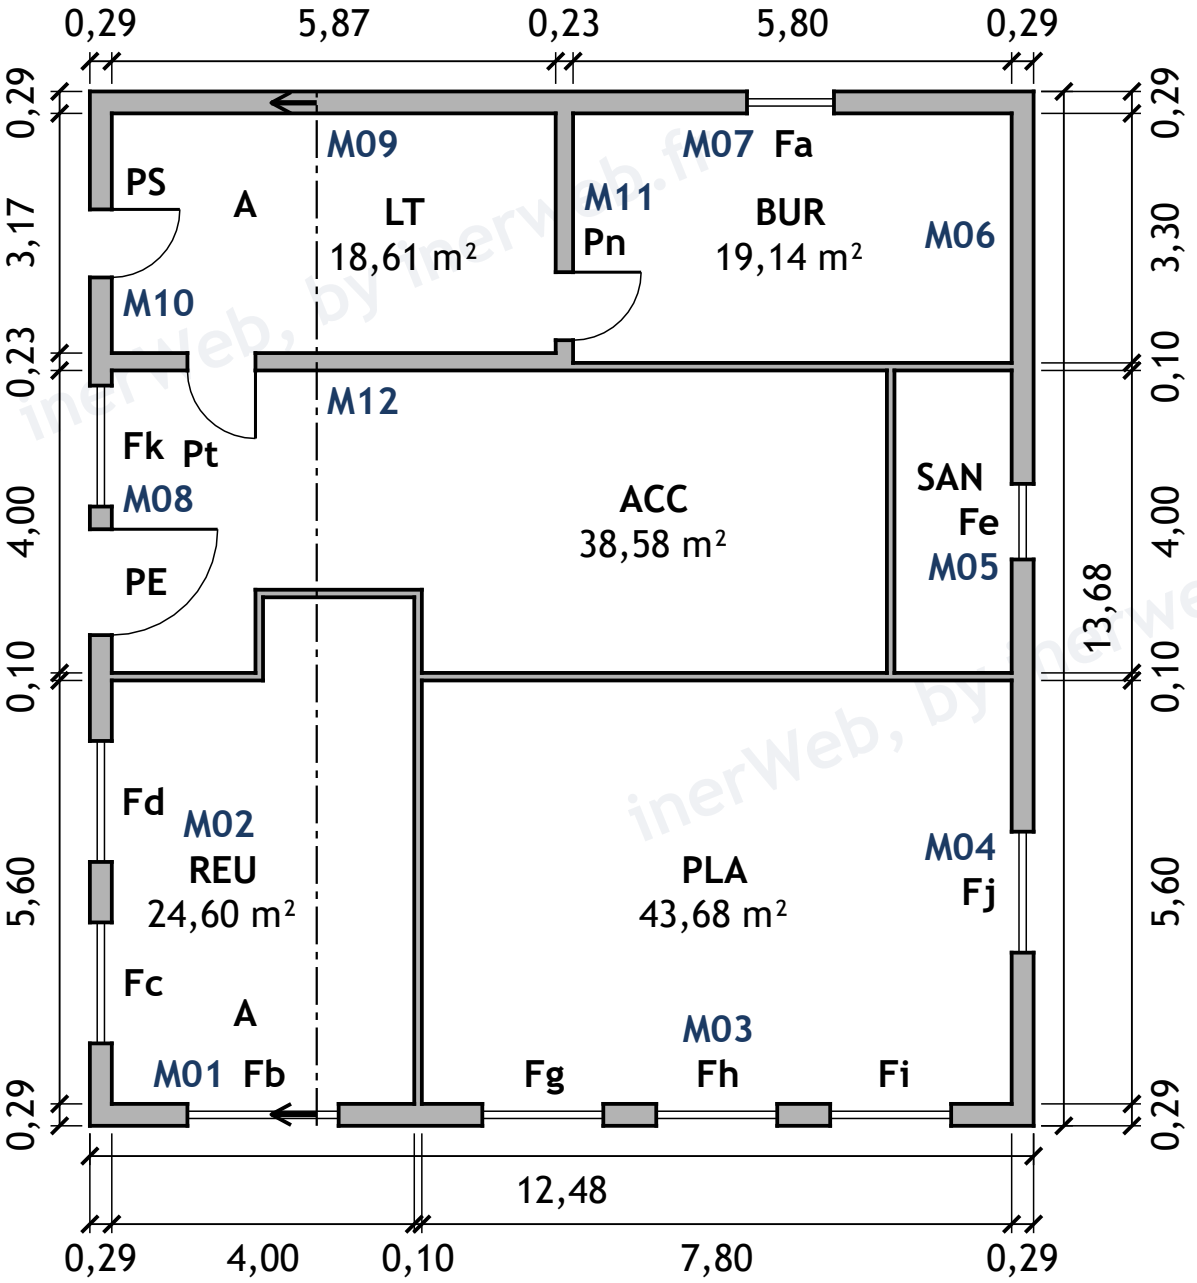


Locaux


REU : Salle de réunion
24,60 m², sous plafond 3,00 m
PLA : Plateau de bureaux
43,68 m², sous plafond 2,60 m
ACC : Accueil et circulation
38,58 m², sous plafond 2,60 m
SAN : Sanitaires
6,20 m², sous plafond 2,60 m
BUR : Bureau
19,14 m², sous plafond 2,60 m
LT : Local technique, non chauffé
18,61 m², sous plafond 2,60 m

Mxx : repère d'un mur
Fx, Px : repère d'une baie
A-A : trace de la coupe

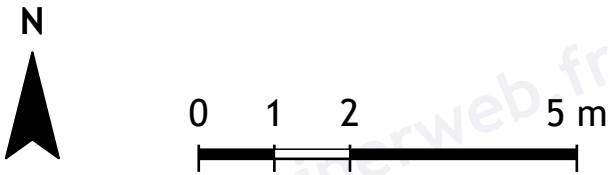

inerWeb, by inerweb.fr


inerWeb | Bureau d'études | **Plan du rez-de-chaussée** | Bureaux d'étude BE, Région parisienne, zone H1a
Échelle 1/100 | Cotes en mètres | 03/11/2026

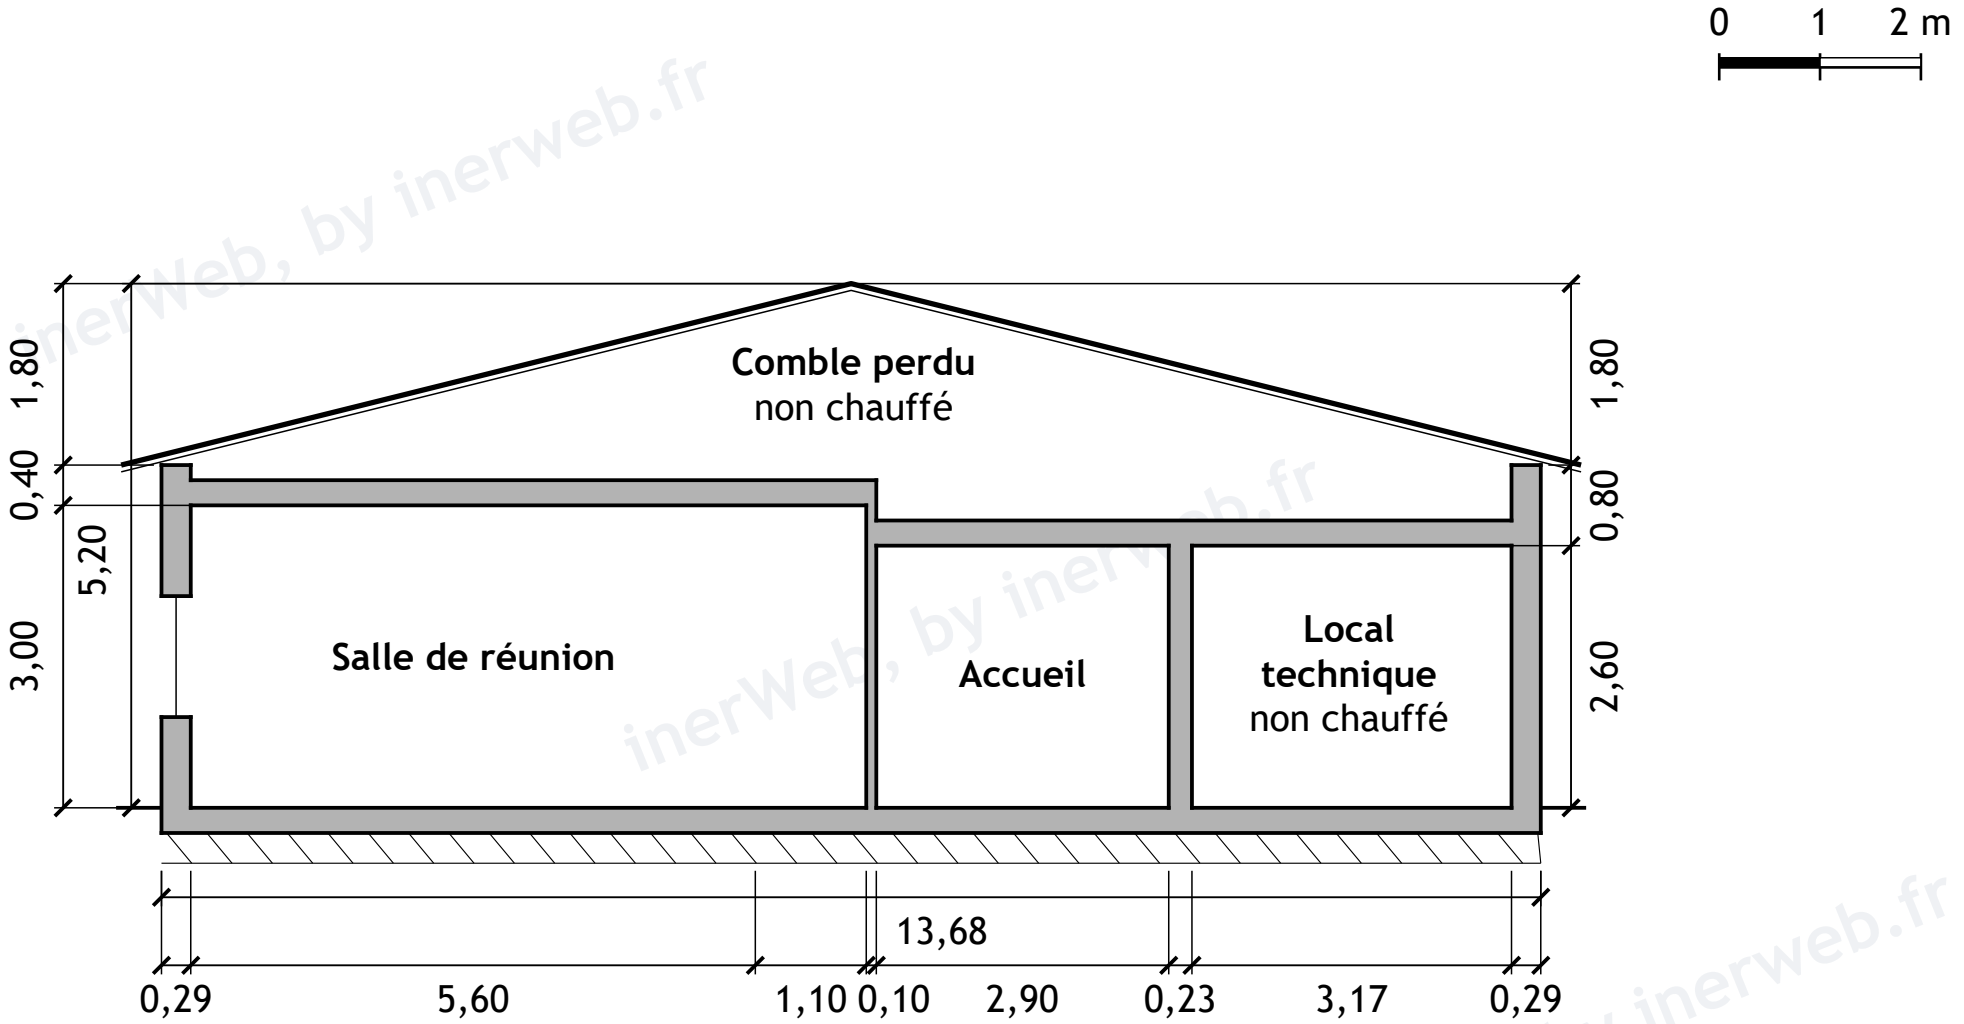


inerWeb, by inerweb.fr

inerWeb **Bureau d'études** **Coupe A-A** Bureaux d'étude BE, Région parisienne, zone H1a

Échelle 1/75 Cotes en mètres 03/11/2026

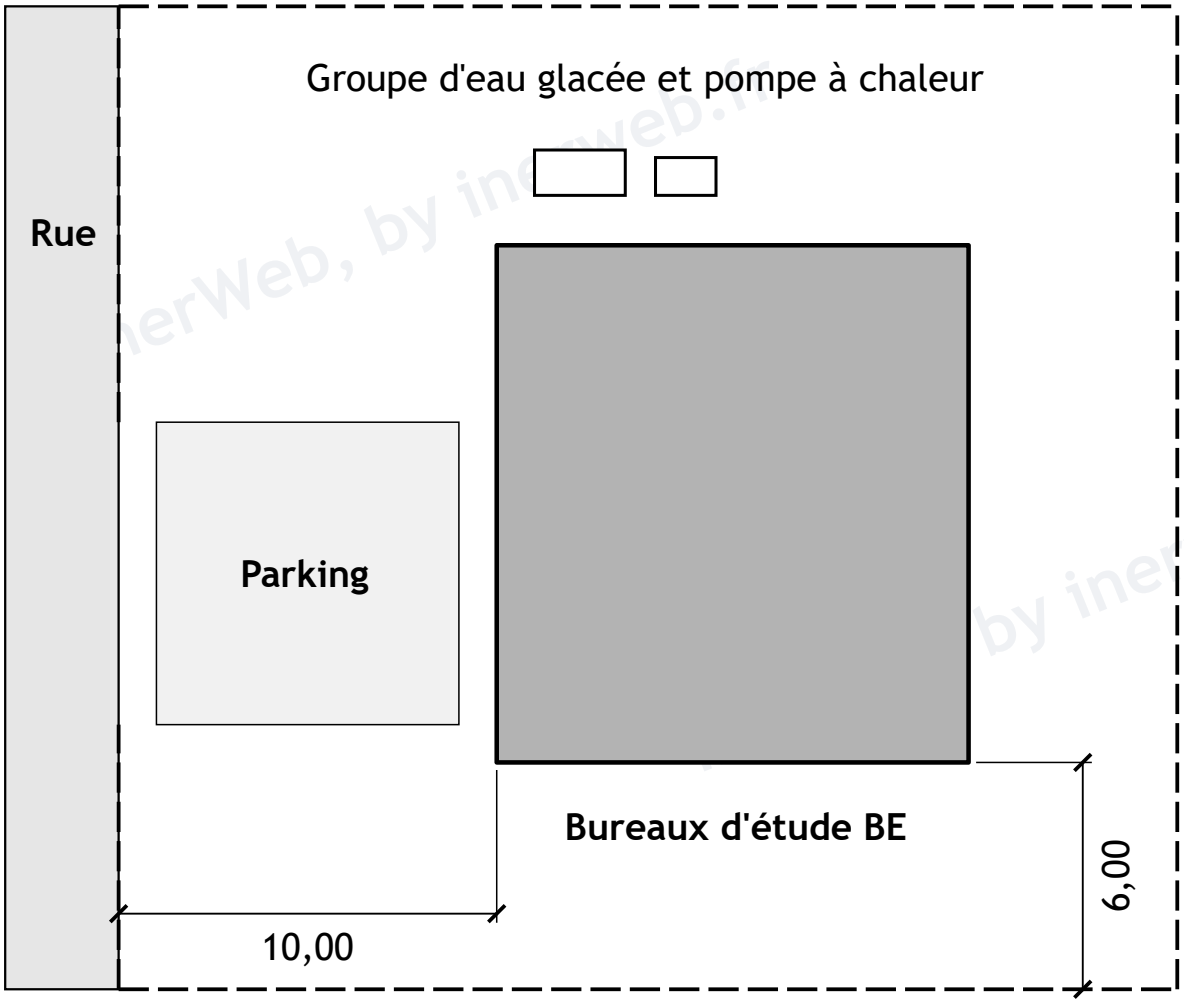



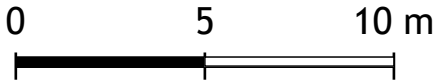

Région parisienne
Zone H1a
Altitude 50 m
Entrée à l'ouest

inerWeb, by inerweb.fr

inerWeb | Bureau d'études | **Plan de masse** | Bureaux d'étude BE, Région parisienne, zone H1a

Échelle 1/200 Cotes en mètres 03/11/2026

Repère	Type	Larg.	Haut.	Allège	Local	Mur	Orient.
Fb	Fenêtre 2 vantaux	2,00	1,20	0,90	Salle de réunion	M01	Sud
Fc	Fenêtre 2 vantaux	1,60	1,25	0,95	Salle de réunion	M02	Ouest
Fd	Fenêtre 2 vantaux	1,60	1,25	0,95	Salle de réunion	M02	Ouest
Fg	Fenêtre 2 vantaux	1,60	1,25	0,90	Plateau de bureaux	M03	Sud
Fh	Fenêtre 2 vantaux	1,60	1,25	0,90	Plateau de bureaux	M03	Sud
Fi	Fenêtre 2 vantaux	1,60	1,25	0,90	Plateau de bureaux	M03	Sud
Fj	Fenêtre 2 vantaux	1,60	1,25	0,90	Plateau de bureaux	M04	Est
Fe	Fenêtre 1 vantail	1,00	0,60	1,60	Sanitaires	M05	Est
Fa	Fenêtre 1 vantail	1,15	1,40	0,90	Bureau	M07	Nord
Pn	Porte pleine	0,90	2,10	0,00	Bureau	M11	Ouest
PE	Porte d'entrée pleine	1,40	2,20	0,00	Accueil et circulation	M08	Ouest
Fk	Fenêtre 2 vantaux	1,60	1,25	0,90	Accueil et circulation	M08	Ouest
Pt	Porte pleine	0,90	2,10	0,00	Accueil et circulation	M12	Nord
PS	Porte de service pleine	0,90	2,10	0,00	Local technique	M10	Ouest

Largeur, hauteur et allège en mètres, dimensions de tableau.
L'allège est la hauteur entre le sol fini et le bas de la baie. Les portes ont une allège nulle.
Orientation : celle de la face extérieure du mur. Les portes entre locaux chauffés ne sont pas relevées.

inerWeb, by inerweb.fr